


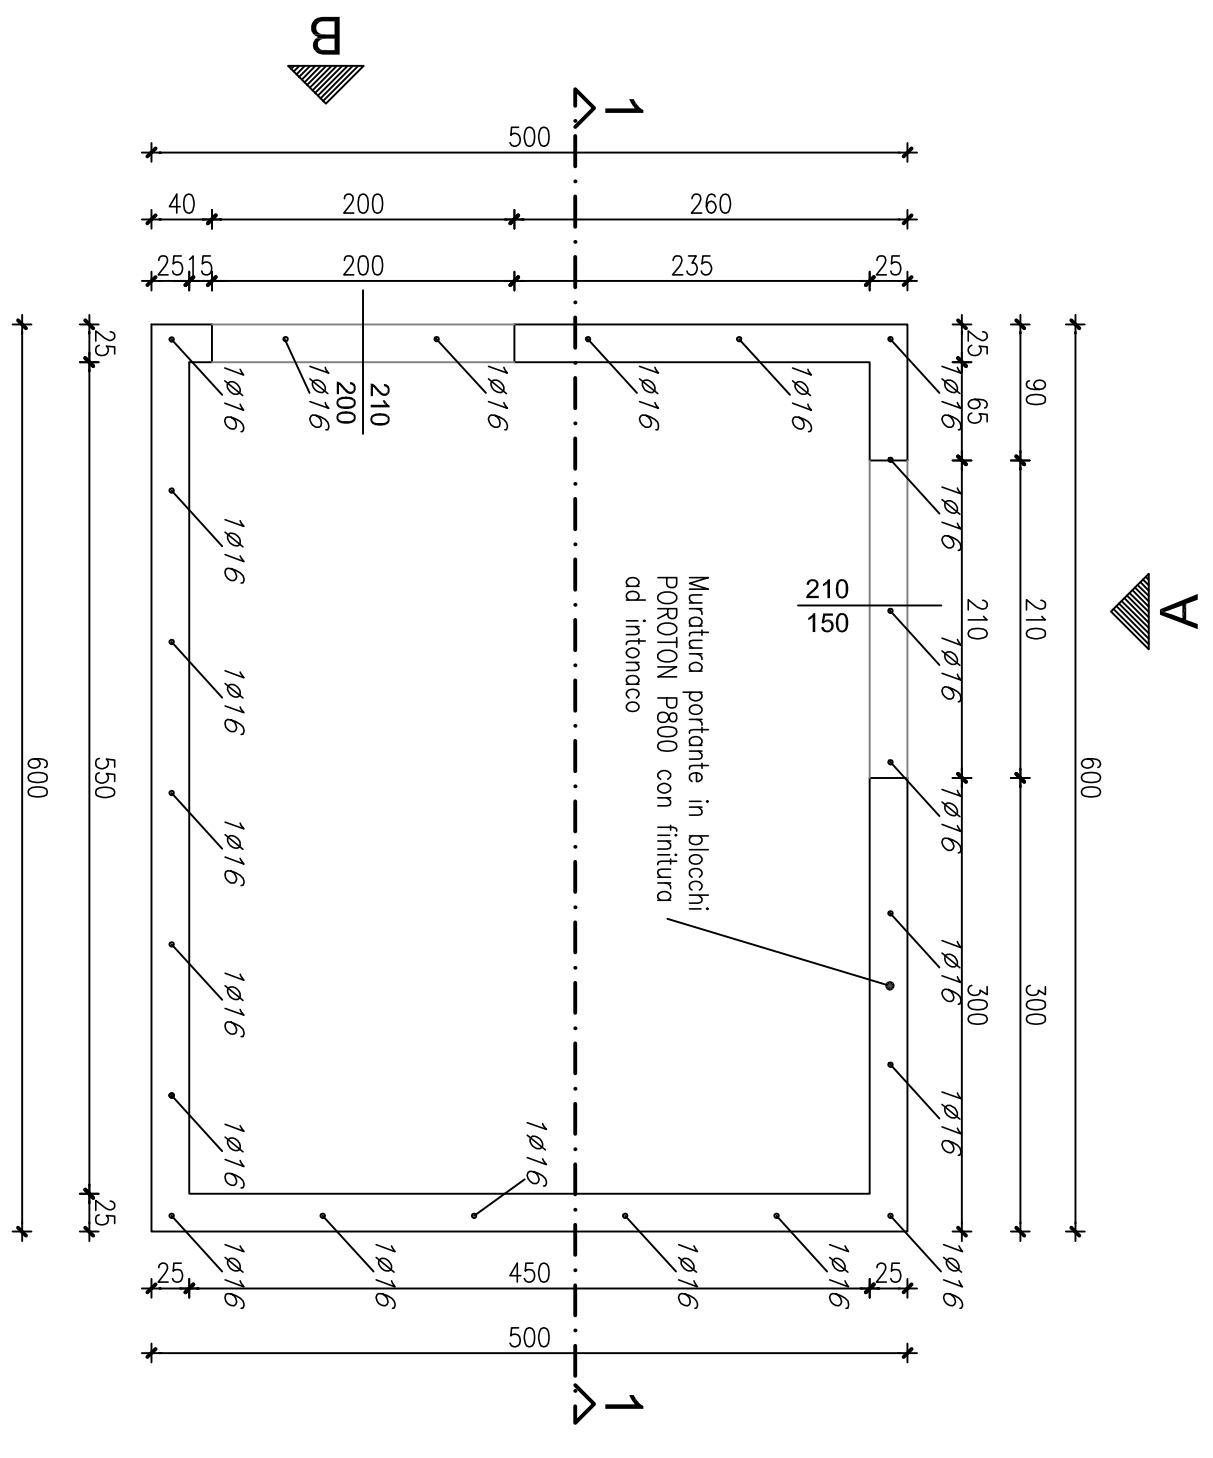


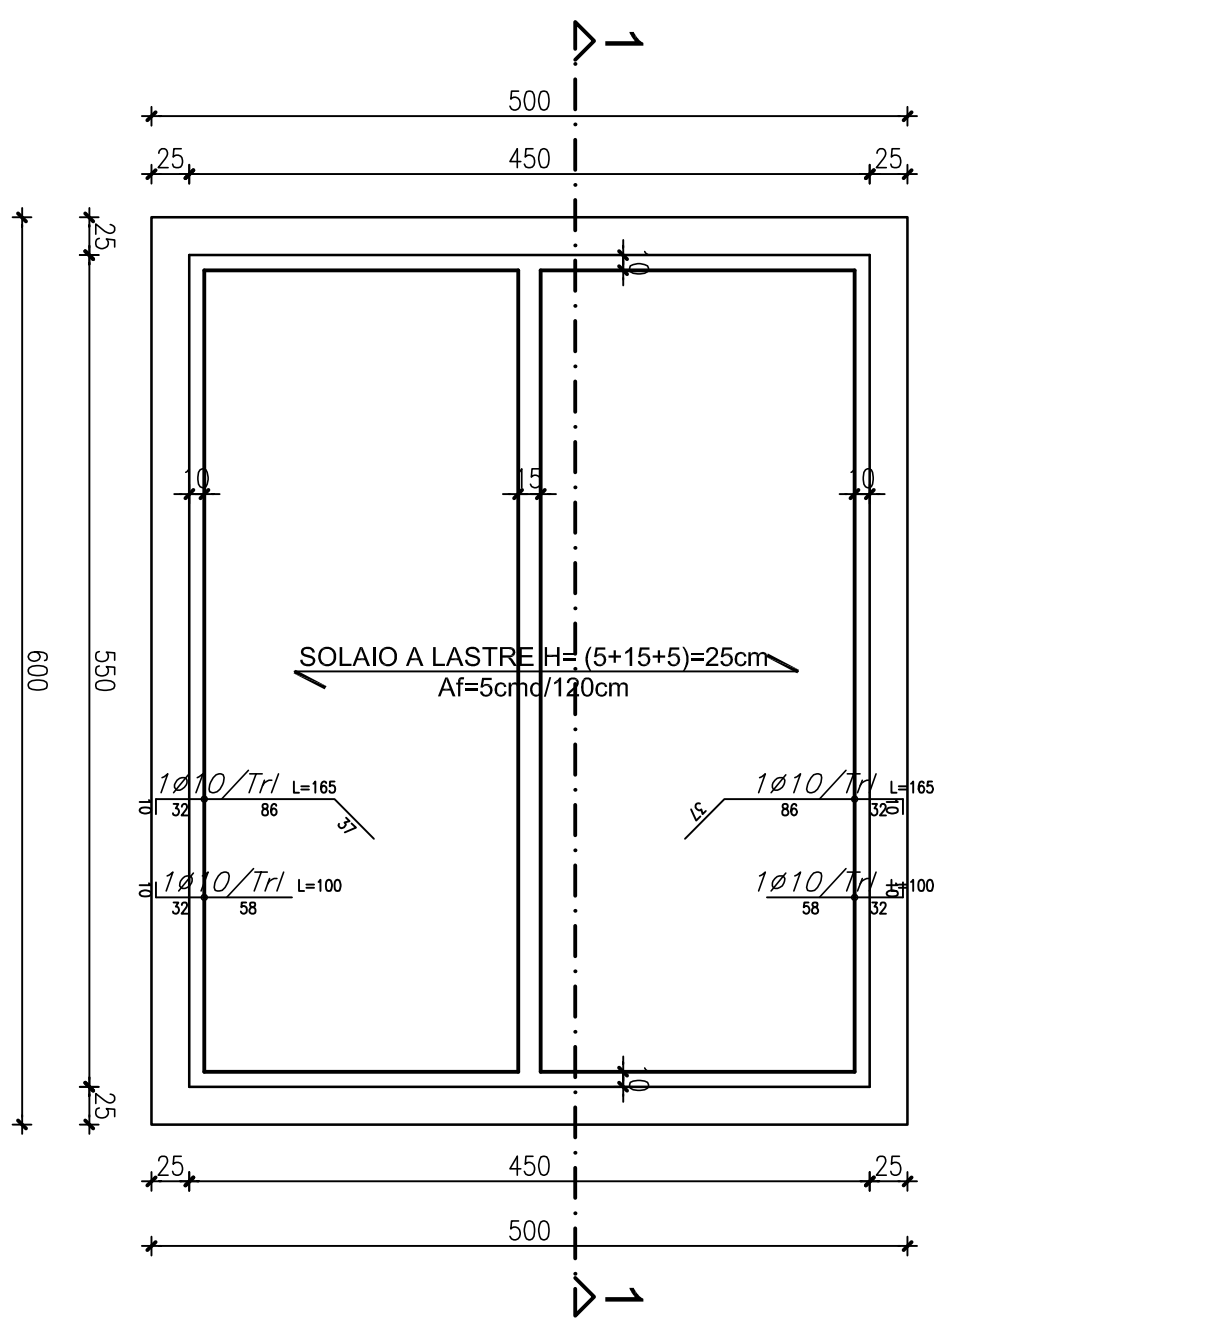


PIANTA
PARETI IN MURATURA

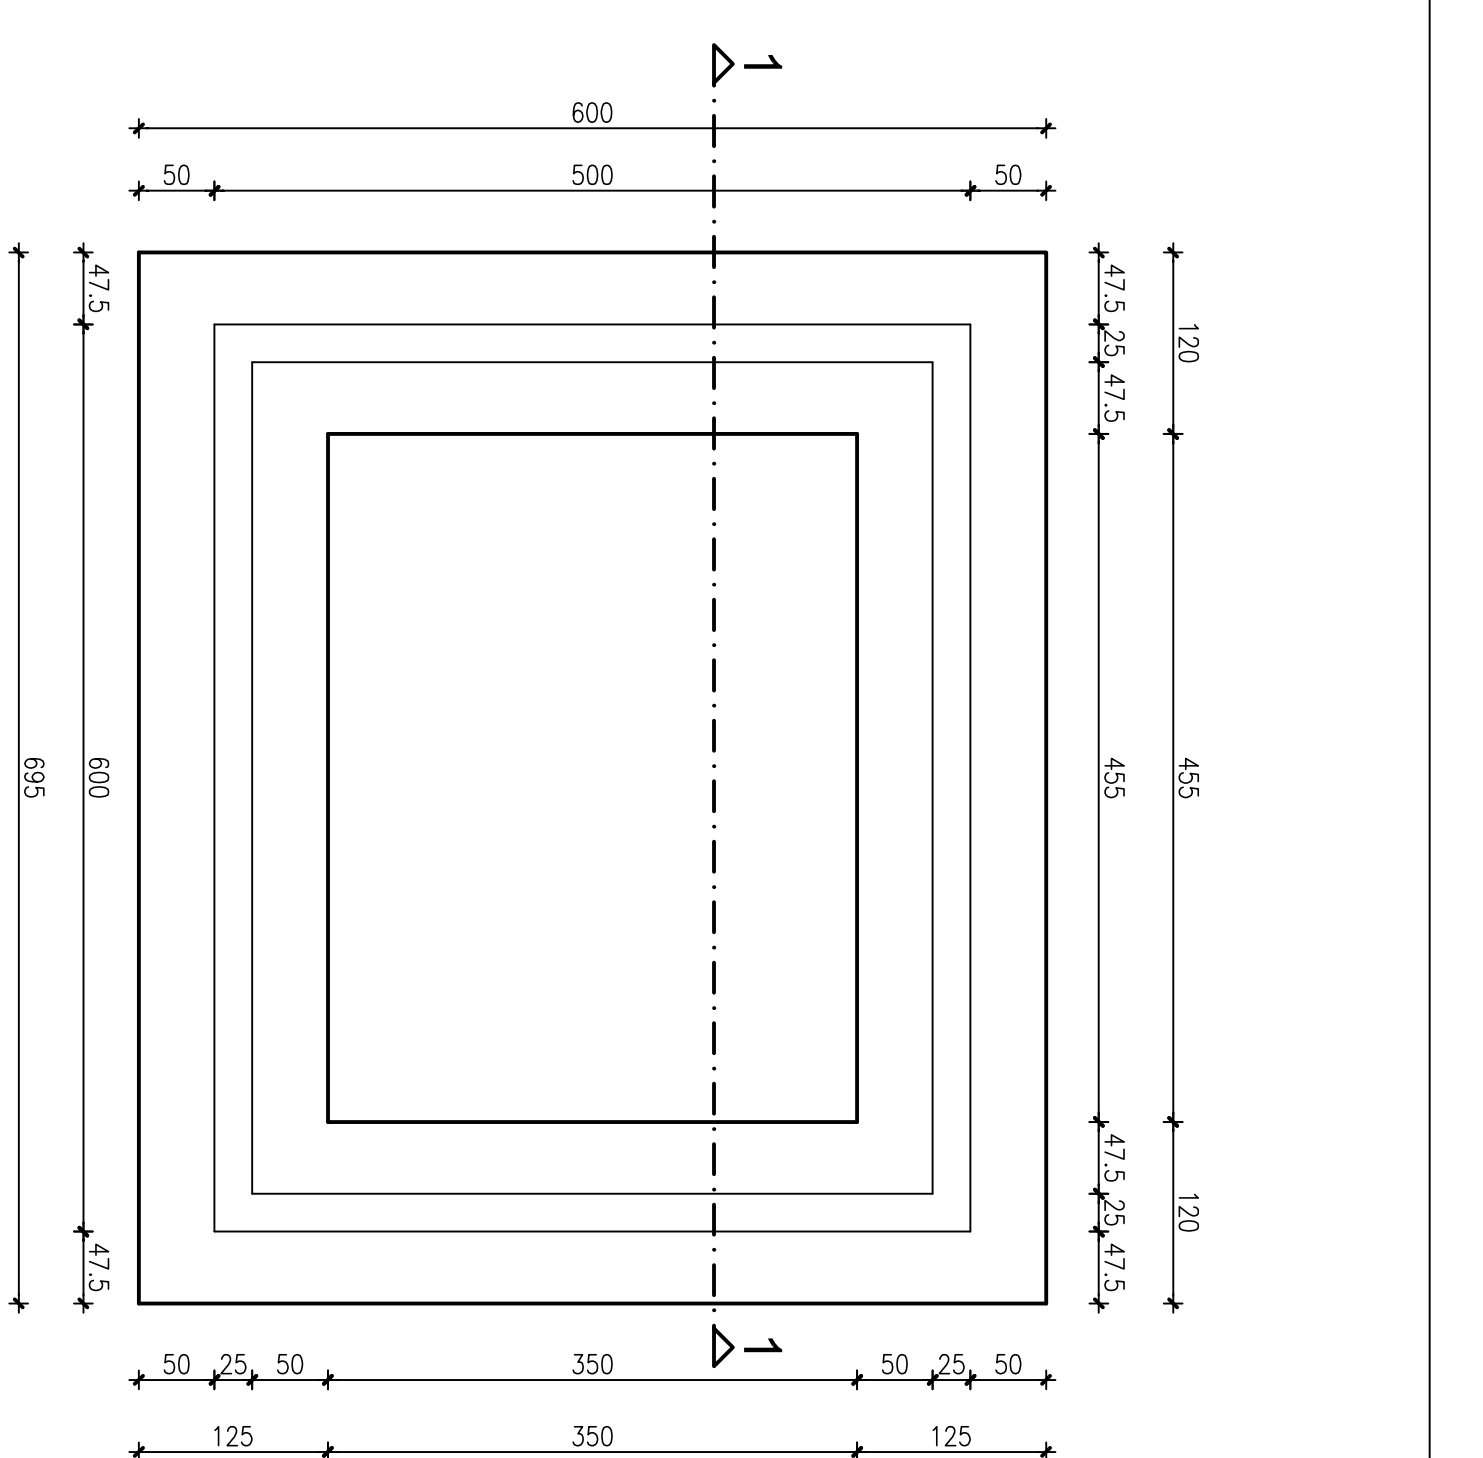


PIANTA COPERTURA

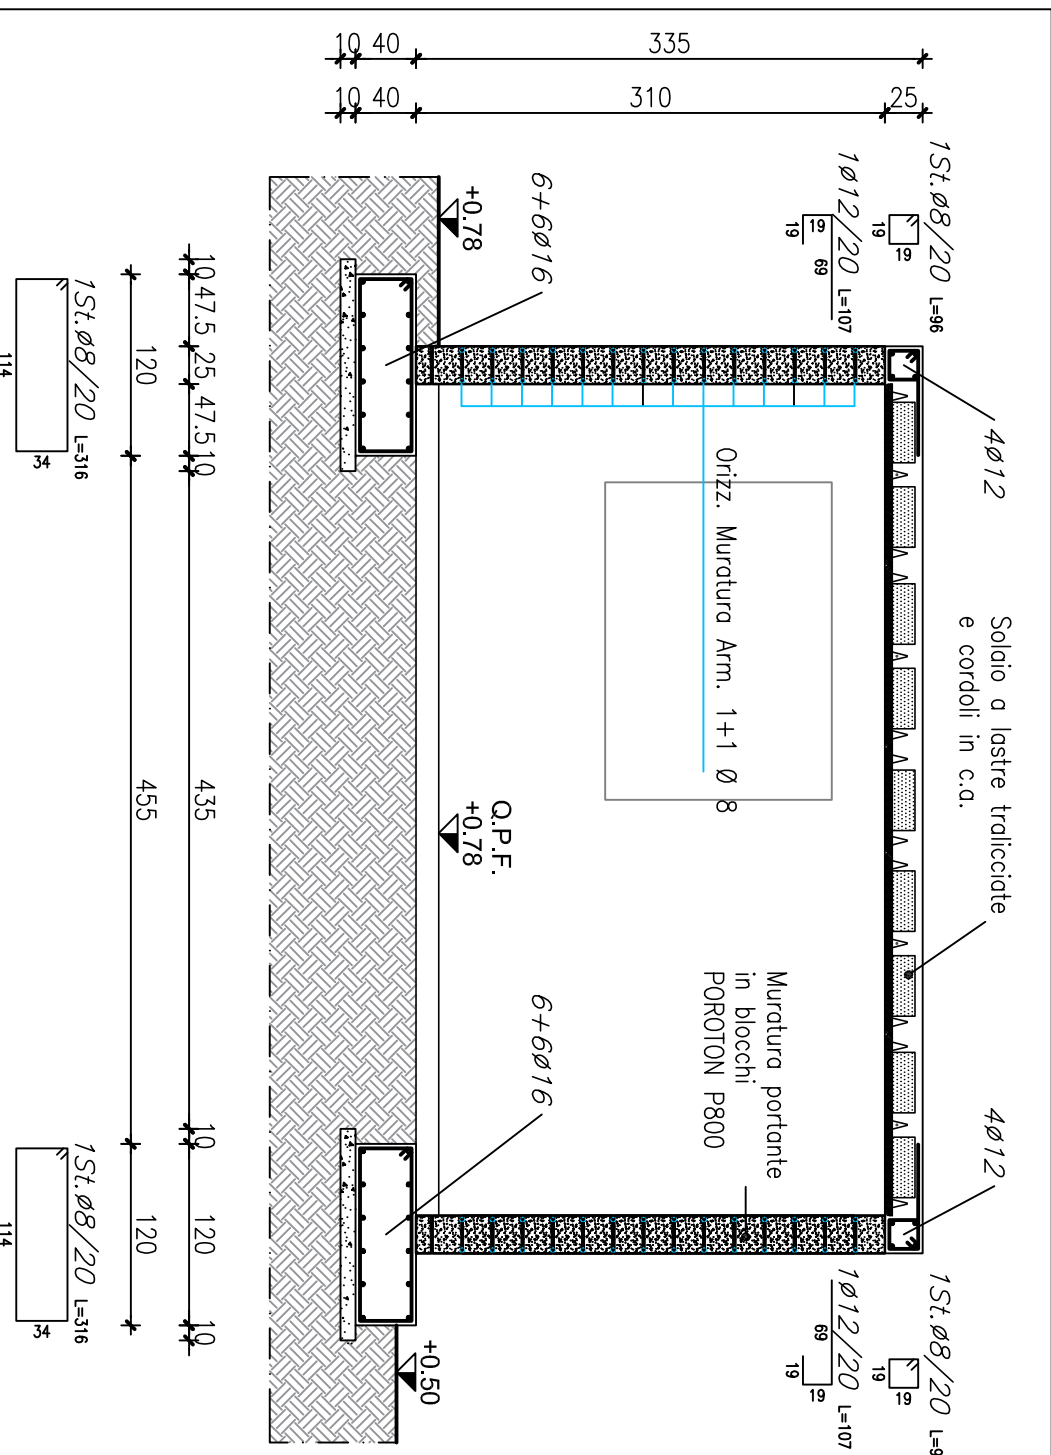


Sezione 1-1

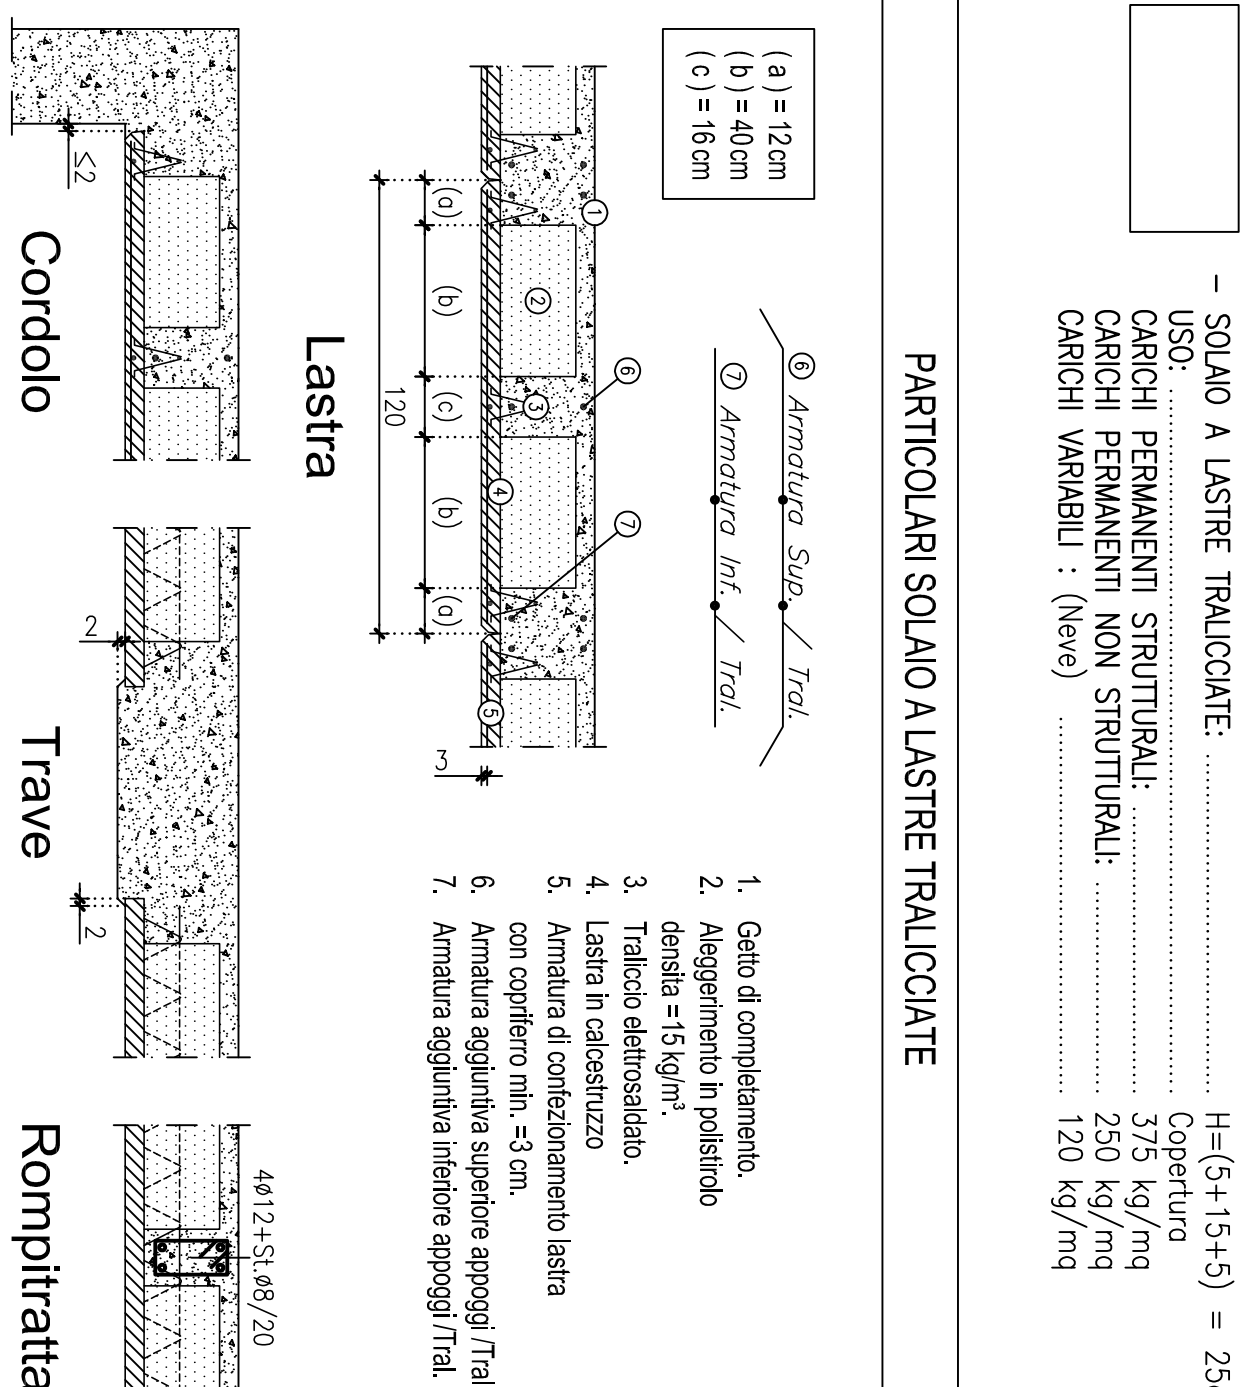

PARTICOLARI SOLAIO A LASTRE TRALICCIAE

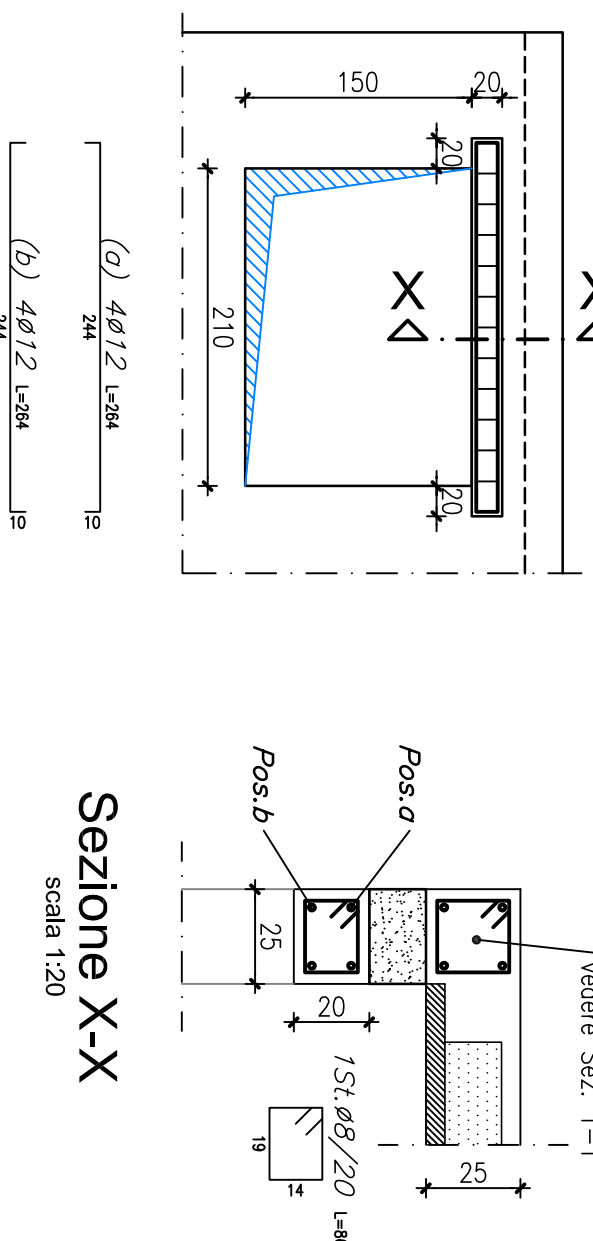

Sezione X-X

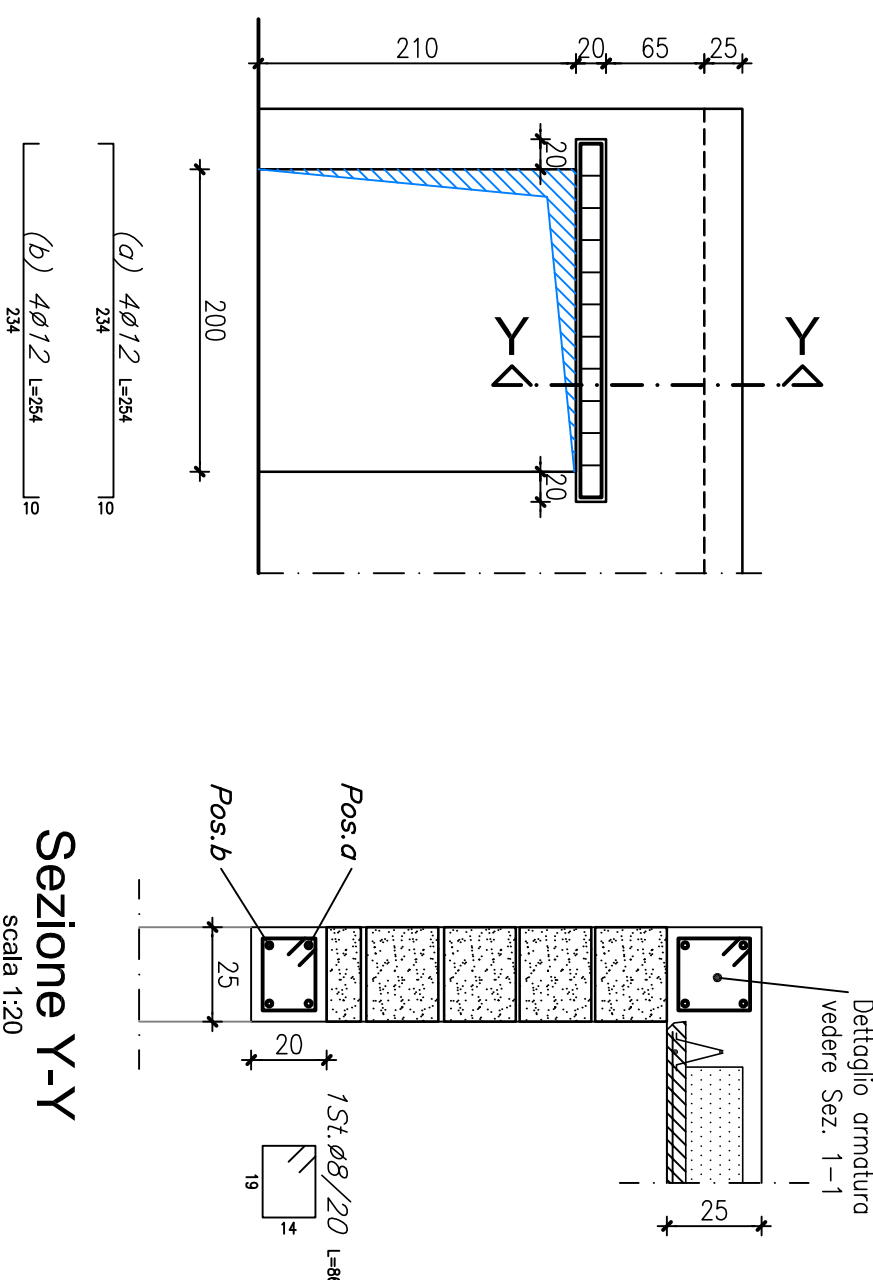

Sezione Y-Y



CALCESTRUZZO PER CEMENTO ARIATO										DISPOSIZIONI DELLA D.L.	
STRUTTURE	Classe di resistenza	Resistenza caratteristica R _{ck}	Capogiro minimo (senza appoggi)	Spessore minimo	Rapporto max. d/c	Classe di esposizione (cl. 22)	Classe di esposizione per parti sotterranee (cl. 22b)	n° di prove	NOTE		
	[N/mm ²]	[N/mm ²]	[mm]	[mm]	[kg/kg]			DIM. [x x] x [x]			
MURONE	C12/15	15	-	-	-	-	-	30	-		
FONDAZIONI	C25/30	30	30	32	0,6	-	-	X/2	-		
ELEVAZIONI	C25/30	30	30	32	0,6	-	-	X/1	-		
TERRI E SODI	C25/30	30	30	32	0,6	-	-	X/1	-		

NOTE:	
1.	CONCILIARE CONDOTTA DEBBO ESSERE POSTI IN OPERA IN ACCORDO ALLE PRESSIONI DEL CARICOLO SPECIALE APPARATI ALI PRIME DELLE VERANTI E ALLA UN EN 12670
2.	L'IMPRESA E TENUTA DA AVVERTIRE IL DIRETTORE DEI LAVORI PRIMA DEL GETTO. IL COSSO E DOPO ESSERE STATO VERIFICATO E CONSTATO CHE NON E' DOPO IL L'IMPRESA E TENUTA A FORMARE IL DIRETTORE DEI LAVORI TUTTA LA DOCUMENTAZIONE DI QUALIFICAZIONE DEL MATERIALE PROPOSTA DALLA NOMINATA VERGINE.
3.	DESENTI NON ESSERE ESCLUSAMENTE PER UNO BILACIO DOTTI DI MARCA/ORA CE IN CONFORMITA' CON LE NORME EUROPEE E NELLE CONDIZIONI DI PROVA.
4.	GLI ACCIDENTI DEVONO ESSERE DI TIPO NATURALE, ARTIFICIALE, OVVERO PROVENIENTI DAL PROCESSO DI RICICO CONTINUI ALLA NOMIA UN EN 12670 E ALTE UN 6820-1 E UN GLI ACCIDENTI DEVONO ESSERE CONTINUI ALLA UN EN 934-2 E PREVENIENTE APPROVATI DALLA D.L.

NOTE PER L'ESECUZIONE DEI PRELIEVI:	
1.	CON PRELIEVO 2 PROVAI DEVONO ESSERE ESSETRIO CALCESTRUZZO CON PRELIEVO UNO MESSIMO DI 100cm DI
2.	CON PRELIEVO DEBO ESSERE IDENTIFICATI IN FORMA INDISTINGIBILE CON GLI ESEMPLI DELL'ETICHETTO
3.	LA PREPARAZIONE, LA FORMA, LE DIMENSIONI E LA STAGIONATURA DEI PROVAI DEBO ESSERE CONFORME EN 12390-2/2009
4.	LE PROVE DI COMPRESIONE SUI PROVAI DEVONO ESSERE ESSETRIO CON PRELIEVO ALLA NOMIA UN EN 12670-1/2012 E UN EN 6820-1
5.	LA PREPARAZIONE DEI PROVAI E LA STAGIONATURA DEI PROVAI DEVONO ESSERE CONFORMI ALLE PREVISIONI DELL'EN 12670-1 E UN EN 6820-1

ACQUARO PER CEMENTO ARMATO			
TIPO	TRONCINI CARATTERISTICHE	SOPRARESTIZIA	ALLINEAMENTO PRELIMI
Se (m/mt)	Rottura I _{se} (m/mt)		(m)
BASIC	450	540	1,155(m)/Kg1,35 > 7,5%

[illegible][illegible]

 Mascheroni e Associati S.r.l. Via S. Maria Maddalena, 10/C/101, 056713249 Fax: 0752525523 post@mascheroniasociati.it	ISTITUTO ZOOPROFIATICO Sperimentale DELLA LOMBARDIA E DELL'EMILIA ROMAGNA	
	SEDE DI LODI	
	Nuovi laboratori ex zona stibudolfi Progetto Esecutivo	
	Strutture Promte, proppetti e sezioni	
scala 1:50-1:20	disegnatore	TAV. 15